APTO PARA CONSTRUCCIÓN
HOSPITAL PROVINCIA CORDILLERA
sacyr INGENIERÍA E INFRAESTRUCTURAS

APROBADO
Por Sergio Fernandez fecha 9:51 , 25/08/2025

HPC
VERSIÓN 1
APTO PARA CONSTRUCCIÓN

Jonathan Cristopher Hervera Álvarez
Firmado digitalmente por Jonathan Cristopher Hervera Álvarez
Fecha: 2025.08.21 14:17:29 -04'00'

Oficina de Atención y Apoyo a Familiares 3.1.4.1.3-1 10,60 m²
Recepción 3.1.4.1.2-1 14,08 m²
Sala de Espera 3.1.4.1.1-1 43,84 m²
Servicio Higiénico Público 3.1.4.1.4-1 4,11 m²
Sala Preparación y Entrega Cadáveres 3.1.4.2.2-1 25,26 m²
CÁMARA CONSERVADORA DE CADÁVERES
Depósito de cadáveres 3.1.4.2.1-1 30,42 m²
Sala Autopsia 3.1.4.2.3-1 41,97 m²
Circulación Interna Morgue CU.3.1.4-1 85,75 m²
Circulación Interna Morgue CU.3.1.4-2 43,02 m²
Sala de Lavado y Secado de Material 3.1.4.3.6-1 12,98 m²
Bodega de Implementos de Aseo (Aseo) 3.1.4.3.7-1 9,94 m²
Bodega de Ropa Limpia 3.1.4.3.12-1 5,32 m²
Bodega insumos no clínicos 3.1.4.3.9-1 5,90 m²
Disponible DI.(-1)-1 2,80 m²
Servicio higiénico del personal 3.1.4.3.2-2 2,66 m²
Vestidor Personal 3.1.4.3.1-1 4,50 m²
Vestidor Personal 3.1.4.3.1-2 4,41 m²
Área Casilleros del Personal 3.1.4.3.10-1 2,47 m²
Servicio Higiénico del Personal (Universal) 3.1.4.3.2-1 5,74 m²
Estar del personal c/kitchenette 3.1.4.3.3-1 18,17 m²
Lavado Camillas 3.1.4.3.4-1 9,84 m²
Recinto Técnico RT.(-1)-1 11,21 m²
Estacionamiento Camillas 3.1.4.3.5-1 10,34 m²
Depósito Transitorio de Ropa Sucia (Ropa Sucia) 3.1.4.3.11-1 5,37 m²
Depósito transitorio de residuos solidos (REAS) 3.1.4.3.8-1 7,97 m²
Vestuarios, duchas y baños personal externo masculino 8.1.4.1.18-1 65,56 m²
Vestuarios, Duchas y Baños Personal Externo Femenino 8.1.4.1.17-1 72,85 m²
Bodega General Insumos Clínicos 8.1.7.1.7-1 105,87 m²
BOD_EQU_Dispensador Horizontal de Medicamentos
CERRAMIENTO DE PROVEEDOR DE EQUIPO DISPENSADOR DE MEDICAMENTOS
Puerta de mantención del proyecto de Bodegas
BOD_EQU_Estanteria Plano de Carga
BOD_EQU_Estanteria Rack Selectivo (h=70cm)
Se considera rebaje de sobrelosa para rieles embutidos de equipos Sistema Full space, de 3 cm.
Bodega General de Medicamentos 8.1.7.1.11-1 219,25 m²
Circulación Troncal Funcionarios CT.F.(-1)-1 50,06 m²
Circulación Troncal Funcionarios CT.F.(-1)-5 7,49 m²
Circulación Troncal Funcionarios CT.F.(-1)-4
Circulación Troncal Funcionarios CT.F.(-1)-16 3,90 m²
Mesón de recepción ropa sucia funcionarios 8.1.4.1.11-1 53,63 m²
Bodega Papelería, Art. Escritorio 8.2.4.2.16-1 7,82 m²
S.H PERSONAL 8.2.4.4.6-1 3,50 m²
Sala Tratamiento Agua 8.2.4.5.14-1 24,42 m²
FRANJA PODOTÁCTIL DE CAUCHO PARA DESNIVELES 3MM. SEGÚN LO ESPECIFICADO EN E.E.T.T. ARQUITECTURA 6.10.5.2.
BALDOSA MICROVIBRADA CIRCUITO NO VIDENTE 40X40. SEGÚN LO ESPECIFICADO EN E.E.T.T. ARQUITECTURA 6.1.2.2
TABLERO ELÉCTRICO
N6P
N5P
N4T
A-EE 01
PFB
D-A-AB
A-BC
A-CD
A-12
A-34

SIMBOLOGIA Y DEFINICIONES

TIPOS DE TABIQUES

T1	T. Opaco común, s/EETT*
T1c	T. Opaco común mayor grosor , s/EETT
TR	T. Revestimiento pilar
T3	T. Delgado para falso, s/EETT
T3a	T. para falso
T3b	T. Grueso para falso
TA	T. Acústico, s/EETT
TV1	T. Vidriado sobre antepecho, s/EETT
TV1e	T. Vidriado sobre antepecho (psiquiatría) s/EETT
TV1mp	T. Vidriado sobre antepecho c/micropersiana, s/EETT
TV2	T. Vidriado de piso a cielo, s/EETT
TV3	T. Vidriado c/ventana alta, s/EETT
TX	T. Opaco Plomado, s/EETT
TF	T. Perimetral Fachada, s/EETT
TF13	Fac. Ventilada (GGCC)
HPL-j	Fac. Ventilada (J.Infantil)
TC	T. Cortafuego, s/EETT
TCa	T. Cortafuego (mayor grosor), s/EETT
TCX	T. Cortafuego plomado, s/EETT
TDS	T. Sepadadores de baños, s/EETT
TM	T. Móvil, s/EETT
TB	T. Blindado, s/EETT
TEa	Panel sanitario de 50 a 80mm
TEb	Panel sanitario de 35 a 80mm
TEc	Panel sanitario con ventana incorporada 20 a 50 mm
TEd	Panel sanitario de revestimiento con ventana incorporada de 20 a 50 mm
■	Muro de Hormigón armado, s/EETT
PUR_100	Paneles frigoríficos (100mm)
PUR_70	Paneles frigoríficos (70mm)

SÍMBOLOS

M1 / CIE / PAV / M3 / M4 / M2 Nombre Recinto Código Recinto Área Recinto	M1,M2,M3,M4: Indica terminación de muro PAV: Indica tipo de pavimento CIE:Indica tipo de cielo
TF10	Indica tipo de tabiques
MX.X.XX	Indica tipo de mobiliario, según criterio de diseño.
NPT X.XX	Indica nivel de piso terminado
NTN X.XX	Indica nivel de terreno natural
PI01a 1' - 0"	Indica tipo de puerta y ancho de vano
▨	Indica línea Cortafuego
▨	Indica tabiques Cortafuegos Plomados
▨	Indica tabiques plomados
▨	Indica tabiques acústico
■	Indica Recorrido Mantenimiento
▨	Indica Impermeabilización
A7	Indica Tipo de Artefactos y Accesorios
EE 04	Indica Código de Escalera
1i	Indica código de Circulación Vertical según Especialidad de Circulaciones Verticales Mecánicas
A1B	Indica código Núcleo de Circulación Vertical según Especialidad de Circulaciones Verticales Mecánicas
XXXX X XXX	Indica código de Cubrejuntas
🟥	Boca de incendios Equipada (BIES) .Gabinetes, según especialidad de Seguridad
PFB	Baños prefabricados (PFB)

NOMENCLATURA DE ÁREAS

🟦	Circ. Troncal de Funcionarios
🟦	Circ. Interna de Unidades
🟥	Circ. Troncal Pública
🟥	Esperas Públicas
🟧	Circ. Restringida
🟨	Circ. Semi-Restringida
🟩	Circ. No Restringida
⬜	R. Disponibles
⬛	R. Técnicos/Datos
🟪	R. Disponibles (Rayos UEH)
🟦	R. Biolimpios
🟦	Estacionamientos

TIPOS DE PUERTAS

Puertas Madera Llena, s/EETT	
PI01a	P. Simple Abatir, hoja de 70cm
PI01b	Idem P01a, hoja de 80cm
PI01c	Idem P01a, hoja de 90cm
PI01d	P. Puertín Abatir, hojas de 90cm y 40cm
PI01e	P. Doble Abatir, hojas de 70cm
PI01f	P. Doble Abatir, hojas de 90cm
PI01g	P. Simple Abatir (psiquiatría), hoja de 90cm
PI01h	P. Simple Abatir (psiquiatría), hoja de 90cm
PI01i	P. Simple Corredera, hoja de 140cm
PI01j	P. Simple Abatir, Hoja de 110cm, Psiquiatría
PI01k	P. Simple Abatir, Hoja de 110cm
PI01l	P. Simple Abatir, Hoja de 120cm
Puertas Madera con Mirilla, s/EETT	
PI02a	P. Simple Abatir, Madera c/mirilla, hoja de 90cm
PI02b	P. Puertín Simple Corredera, hojas de 90-40cm
PI02c	P. Puertín Simple Corredera, hojas de 90-40cm (psiquiatría)
PI02d	P. Puertín Simple Corredera, hojas de 90-40cm (psiquiatría contención)
Puerta Plomadas, s/EETT	
PI03a	P. Simple Abatir Plomada, hoja de 70 cm
PI03b	P. Simple Abatir, Madera Plomada, hoja 90cm
PI03c	P. Doble Abatir, Madera Plomada, hojas 70/70cm
PI03d	P. Doble Abatir, Madera Plomada, hojas 90/90cm
Puertas Metalicas Vidriadas, s/EETT	
PI04a	P. Simple Abatir, hoja 90cm
PI04b	P. Puertín Abatir, hojas 90-40cm
PI04c	P. Simple Vaivén, hoja 90cm
PI04d	P. Doble Vaivén, hoja 90cm
PI04e	P. Simple Abatir, hoja de 100 cm
PI04f	P. Doble Abatir, hojas 90/90cm
PI04g	P. Puertín Abatir, hojas 80-80cm
PI04h	P. Doble Vaivén, hojas 80/80cm
PI05a	P. Corredera c/Zócalo, hoja 190cm
PI05b	Idem P05a, hoja 140cm
Puertas Automaticas HPL, s/EETT	
PI06a	P. Corredera, hoja 140cm
PI06b	Idem P06a, hoja 190cm
PI06c	Idem P06a, hoja 160cm
Puertas de Escape, s/EETT	
PI07a	P. Simple Escape, RF120, hoja 120cm
PI07b	P. Doble Escape, RF120, hojas 80cm
PI07c	P. Doble Escape, RF120, hojas 90cm
PI07d	P. Doble Escape, RF120, hojas120cm
Puertas Cortafuego, s/EETT	
PI08a	P. Simple, RF120, hoja 90cm
PI08b	P. Simple, RF120, hoja 120cm
PI08c	P. Doble, Bidireccional, RF120, hojas 90cm
PI08d	P. Doble, Unidireccional, RF120, hojas 90cm
PI08e	P. Doble, Bidireccional, RF120, hojas 120cm
PI08f	P. Doble, Unidireccional, RF120, hojas 120cm
PI08g	P. Doble, Unidireccional, RF120, hojas 90cm
PI08h	P. Simple,110cm
Puertas Resistentes al Fuego, s/EETT	
PI09a	P. Simple Abatir, RF60, hoja 70cm
PI09b	P. Simple Abatir, RF60, hoja 80cm
PI09c	P. Simple Abatir, RF60, hoja 90cm
PI09d	P. Simple Abatir, RF120, hoja 90cm
PI09e	P. Doble Abatir, RF60, hojas 90/40cm
PI09f	P. Doble Abatir, RF120, hojas 90/40cm
PI09g	P. Doble Abatir, RF60, hojas 70/70cm
PI09h	P. Doble Abatir, RF120, hojas 70/70cm
PI09i	P. Doble Abatir, RF120, hojas 90/90cm
PI09j	P. Simple Abatir, RF120, hoja de 110cm
PI09k	P. Doble Abatir, RF60,hoja de 110cm
PI09l	P. Doble Abatir, RF60,hoja de 90cm, Psiquiatría
Puertas de HPL (Baterias de baños y vestidores), s/EETT	
PI10a	P. Simple, hoja 60cm
PI10b	P. Simple, hoja 70cm
PI10c	P. Simple, hoja 90cm
Puerta de Alto Tráfico, s/EETT	
PI11a	P. Doble Vaivén, hojas 70/70cm,
PI11b	P. Simple Abatir, hoja 90cm
Puertas de Seguridad, s/EETT	
PI12a	P. Simple Abatir, Blindada, hoja 100cm
Puertas de Mezclas Estériles, s/EETT	
PI13a	P. Simple Abatir, hoja 90cm
PI13b	P. Simple, hoja 100cm
Puertas Técnicas (Metálicas Llenas), s/EETT	
PT01a	P. Doble Abatir, RF90, hojas 60/60cm
PT01b	P. Doble Abatir, RF120, hojas 60/60cm
PT01c	P. Doble Abatir, RF120, hojas 90/90cm
PT01d	P. Doble Abatir, RF120, hojas 90/90cm
PT01e	P. Simple Abatir (Registro), hoja 60cm
Puerta para Residuos	
PT01f	P. Doble, hojas de 70/70 cm
Puerta para Estanques	
PT01g	P. para estanques
PT01h	P. Doble Abatir, RF60, hojas 80/80cm
PT01i	P. Simple Abatir, RF120, hoja 90cm
Puertas Exteriores Vidriadas de aluminio c/RPT, s/EETT	
PE01a	P. Simple Abatir, hoja 90cm
PE01b	P. Simple Abatir (psiquiatría),hoja 90cm
PE01c	P. Doble Abatir, hojas 80cm
PE01d	P. Doble Abatir, hojas 90cm
PE01e	P. Doble Abatir (para muro cortina),hoja 90cm
PE01f	P. Simple Abatir, hoja 90cm
Puertas Exteriores Vidriadas de acceso, s/EETT	
PE02a	P. Doble Corredera, hojas 85cm
PE02b	P. Doble Corredera, hojas 90cm

TIPOS DE VENTANAS Y TABIQUES VIDRIADOS

LU1	Claraboya 1200x1200
LU2	Claraboya 1200x1800 Psiquiatría
TV1	Tabique Vidriado
TV1E	Tabique Vidriado Psiquiatría
TV1E'	Tabique Vidriado para Sala Reunión
TV1MP	Tabique Vidriado
TV2	Tabique Vidriado
TV3	Tabique Vidriado
TV4	Tabique Vidriado
VE01a	Corrida Psiquatría 900x2000
VE01b	Corrida Psiquatría 500x1460
VE01c	Corrida Psiquatría 1000x1460
VE01d	Corrida Psiquatría 1500x1460
VE01e	Corrida Psiquatría 2000x1460
VE01f	Corrida Psiquatría 2750x1460
VE01g	Corrida Psiquatría 3000x1460
VE02	Hospitalización 3000 X 2050
VE03a	Plomo Interior 500x1460
VE03b	Plomo Interior 1000x1460
VE03c	Plomo Interior 1500x1460
VE03d	Plomo Interior 2000x1460
VE03e	Plomo Interior 3000x1460
VE03f	Plomo Interior 2500x1460
VE04a	Plomo Exterior 500x1460
VE04b	Plomo Exterior 1000x1460
VE04c	Plomo Exterior 1500x1460
VE04d	Plomo Exterior 2000x1460
VE04e	Plomo Exterior 3000 X 1460
VE05	3000 X 2050
VE06	7400 X 1450
VE07a	2000x900
VE07b	2000x900
VE08	600 X 1000
VE09a	Hall Superior 600 X 1550
VE09b	Hall Superior 600 X 1900
VE09c	Hall Superior 600 X 2600
VE09d	Hall Inferior 600 X 2700
VE09e	Hall Inferior 600 X 3000
VE10	Plaza Hundida
VE11a	Jardin Infantil
VE11b	Jardin Infantil
VE12a	Multicultural 406x1830
VE12b	Casetas De Guardia 1200x1000
VE12c	Casetas De Guardia 400x600
VE12d	Casetas De Guardia 1200x2000
VI01a	Ventana Plomada 700x700
VI01b	Ventana Plomada 1800x700
VI02	Ventana Plomada Tac 90x200
VI03	Ventana Pasamuros 600
VI04	Ventana Pasamuros 1200
VI05a	Ventana Espejo 2700x1200
VI05b	Ventana Espejo 3500x1200
VT1	Transfer De Materiales Doble
VT2	Transfer De Materiales Simple

TIPOS DE MUROS CORTINA

MC01a	Muro Cortina - Fachada Poniente
MC01b	Muro Cortina - Fachada Poniente
MC02a	Muro Cortina Hall Principal - Fachada Sur
MC02b	Muro Cortina Hall Principal - Fachada Sur
MC02c	Muro Cortina Hall Principal - Fachada Sur
MC02d	Muro Cortina Hall Principal - Fachada Sur
MC03	Muro Cortina Hall Principal - Fachada Norte
MC03b	Muro Cortina Hall Principal - Fachada Norte
MC04	Muro Cortina - Fachada Oriente
MC04b	Muro Cortina - Fachada Oriente
MC04c	Muro Cortina - Fachada Oriente
MC04d	Muro Cortina - Fachada Oriente
MC04e	Muro Cortina - Fachada Oriente
MC05a	Muro Cortina - Fachada Norte
MC05b	Muro Cortina - Fachada Norte
MC06a	Muro Cortina Multicultural - Fachada Norte
MC06b	Muro Cortina Multicultural - Fachada Poniente
MC07a	Muro Cortina - Fachada Norte (S01)
MC07b	Muro Cortina - Fachada Oriente (S01)
MC07c	Muro Cortina - Fachada Oriente (S01)
MC08	Muro Cortina Jardín Infantil - Fachada Poniente
Q1	Quebravista Hall
Q2	Estructura Quebravista Hall
Q3	Estructura Metálica Soporte Clima
CE1	Celosías y lamas cerámicas
CE2	Celosía horizontal

TIPOS DE ARTEFACTOS Y ACCESORIOS

Lavamanos s/EETT	
A1	Lavamano clínico
A2	Lavamano clínico c/pedal
A3	Lavamano clínico antivandálico
A4	Lavamano no clínico
A7	Lavamano no clínico, acceso universal
A10	Lavamano baños hospitalización
A11	Lavado quirúrgico porcelana
Lavaderos s/EETT	
B1	L. profundo individual encastrado
B2	L. profundo individual c/estructura propia
B3	L. profundo doble c/estructura propia
B6	L. profundo c/decantador de yeso
B8	Pileta de aseo c/ducha
B9	Lavamanos c/pedal a rodilla
B10	L. Triple
Tinas y Duchas s/EETT	
C2	Tina fierro fundido (para niño)
C4	Receptáculo ducha paciente
C5	Receptáculo ducha personal
C6	Receptáculo ducha psiquiatría
C7	Tina fierro fundido (psiquiatría)
C8	Ducha emergencia c/lavaojos
C9	Ducha en obra prefabricada
Wc y Urinarios s/EETT	
D1	WC fluxor expuesto
D3	WC descarga piso c/fluxor oculto.
D4	WC niño descarga piso c/fluxor expuesto
D5	WC descarga piso c/fluxor oculto (universal)
D6	WC suspendido con fluxor oculto
D8	Bota aguas clínico con ducha manual
D9	Urinario c/fluxor electrónico
D10	WC antivandálicos, pacientes psiquiatricos
Otros Artefactos s/EETT	
E1	Ducha pulsante en WC
E2	Llave de pre-lavado
E3	Pileta o rejilla de descarga
E4	Lavado de Filtros
E5	Llave empotrada
Accesorios s/EETT	
F1	Mudador
F2	Barras de acceso universal (WC)
F3	Barras de acceso universal (duchas)
F4	Secador de manos
F5	Barra cortina de baños
F6	Percheros
F7	Espejo mural
F8	Mudador adulto

TERMINACIONES

10	Estuco Grano Perdido
11	Esmalte al Agua Asepsia Baja
12	Esmalte al Agua hospitalario Asepsia Media
13	Pintura en base Epóxica Asepsia alta
14	Porcelanato Técnico
15	Porcelanato Técnico hasta H=90cm+Pintura
16	Laminado de Alta Presión(HPL)
17	Revestimiento Acolchado Presión
18	Acero Inoxidable Bruñido
19	Revestimiento Acústico de Madera
20	Panel PUR 100
21	Panel PUR 70
23	Panel Lateral Acrílico Esp=16 mm
24	Terminación sanitaria FRP retardante a la llama con color incluido.

CIELOS

200	Losa Revocada en Yeso para Pintura
201	C. Falso Fijo de yeso-cartón Recintos Secos(ST)
202	C. Falso de yeso-cartón Recintos Húmedos (RH)
203	C. Modular de yeso revestido en Vinílico de 24" y 48"
204	C. Modular de yeso revestido en Vinílico c/cenefa
205	C. Mixto Modular de yeso Revestido en Vinilo y cielo de yeso-cartón
206	C. Modular Acústico bandeja Chapa Perforada metálica c/cenefa
207	C. Modular de Madera Acústico
208	C. Modular Fibra Mineral Acústico
209	C modular acústico Owa flexo (Acustico 1)
210	C. modular acústico Owa Humancare (Acustico 2)
211	C. liso Volcanita acústica Rigitone 8-18 (Acustico 3)
213	C. modular acústico Owa Opus (Acustico 4)
214	C. Metálico para exteriores
215	C. autoportante de panel PUR 100 mm
216	C. autoportante de panel PUR 70 mm
217	C. con placas termoaislantes con núcleo de lana de roca y caras de acero galvanizado pre pintado 0,6 mm
218	C. modular acústico Owa flexo c/cenefa
219	C. mixto modular acústico Owa Humancare y cielo de yeso cartón
220	C. modular acústico Owa Opus c/cenefa

Códigos Especiales

S/E	Terminación según Especialidad o Proyecto Especial
N/A	No Aplica

CANALETAS PORTAINSTALACIONES

CPI1	CPI Cuidados Básicos
CPI2	CPI Cuidados Medios
CPI3	CPI Cuidados Medios (Doble)
CPI4	CPI Vertical
ACC1	Riel Portasuero
ACC2	Riel Cortina Separadora
ACC3	Cortina Separadora

PAVIMENTOS

100	Hormigón Pulido Helicoptereado
101	Baldosa Microvibrada Lisa Blanca
102	Porcelanato Técnico
103	Pav. Vinílico Acústico 3,7mm
104	Pav. Vinílico Antiestático 2,0mm
105	Pav. Vinílico Homogéneo 2,0mm
106	Pav. Vinílico Antideslizante R10 2,0mm
107	Pav. Vinílico Antideslizante clase 3 rugoso 2,5mm
108	Pavimento caucho virgen 3mm
109	pavimento caucho virgen disipativo 3mm
110	Pav. Caucho Virgen 4mm
111	Pav. Caucho Virgen Antideslizante para Escaleras
112	Textil Flocado 4,3mm
113	Pisos Elevados para R.Técnicos(grating) sobre terminación esmalte para piso(115)
114	Piso Técnico Elevado H=500mm
115	Esmalte epóxica para piso
116	Resina de Poliuretano para Piso
117	Sector patio de maniobras
118	Limpiapiés embutido metálico
119	Pavimento de panel frigorífico 100 mm
120	Pavimento de panel frigorífico 70 mm
123	Retorno resina de poliuretano 15 cms.
124	Pintura reflectante demarcación de tráfico

CUADRO DE REVISIONES

REV.	FECHA	DESCRIPCIÓN
Rev00	30-06-2023	APTO PARA CONSTRUCCION
Rev01	21-03-2025	ORD 1742 - ALINEACIÓN DE PASILLOS Y TRASDOSADOS
Rev01_V1	13-08-2025	RESPUESTA RDI HPC-UT-SSMSO N°07

Servicio de Salud Metropolitano Sur Oriente
Región Metropolitana
Ministerio de Salud

GOBIERNO DE CHILE
MINISTERIO DE SALUD
SERVICIO METROPOLITANO DE SALUD
SUR-ORIENTE

DISEÑO Y CONSTRUCCIÓN HOSPITAL PROVINCIA CORDILLERA

ETAPA PROYECTO:
ETAPA DE OBRA

EMPLAZAMIENTO:

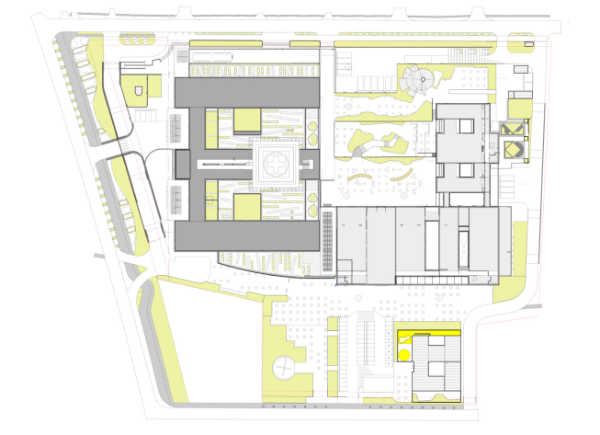

CONTRATISTA:
UTP SACYR HOSPITAL PROVINCIA CORDILLERA
sacyr INGENIERÍA E INFRAESTRUCTURAS

ARQUITECTO JEFE PROYECTO:
MARIANO ALVARO PRIETO LINDHOLM
Firmado digitalmente por MARIANO ALVARO PRIETO LINDHOLM
ALVARO PRIETO LINDHOLM
ARQUITECTO

FIRMA ITOs:
JONATHAN HERVERA ÁLVAREZ
INSPECTOR TÉCNICO DE OBRAS EN SALUD

ESPECIALIDAD:
ARQUITECTURA

CONTENIDO:
PLANTA DE NIVEL -1-A

ORIENTACIÓN:

FECHA: 13 AGOSTO 2025
ESCALA: 1:50

LÁMINA:
HPC-ARQ-PLA-S01-A-501-Rev01_V1

ARCHIVO:
HPC-BIM-ARQ-GEN-XXX-AZ0-M2D-Rev00