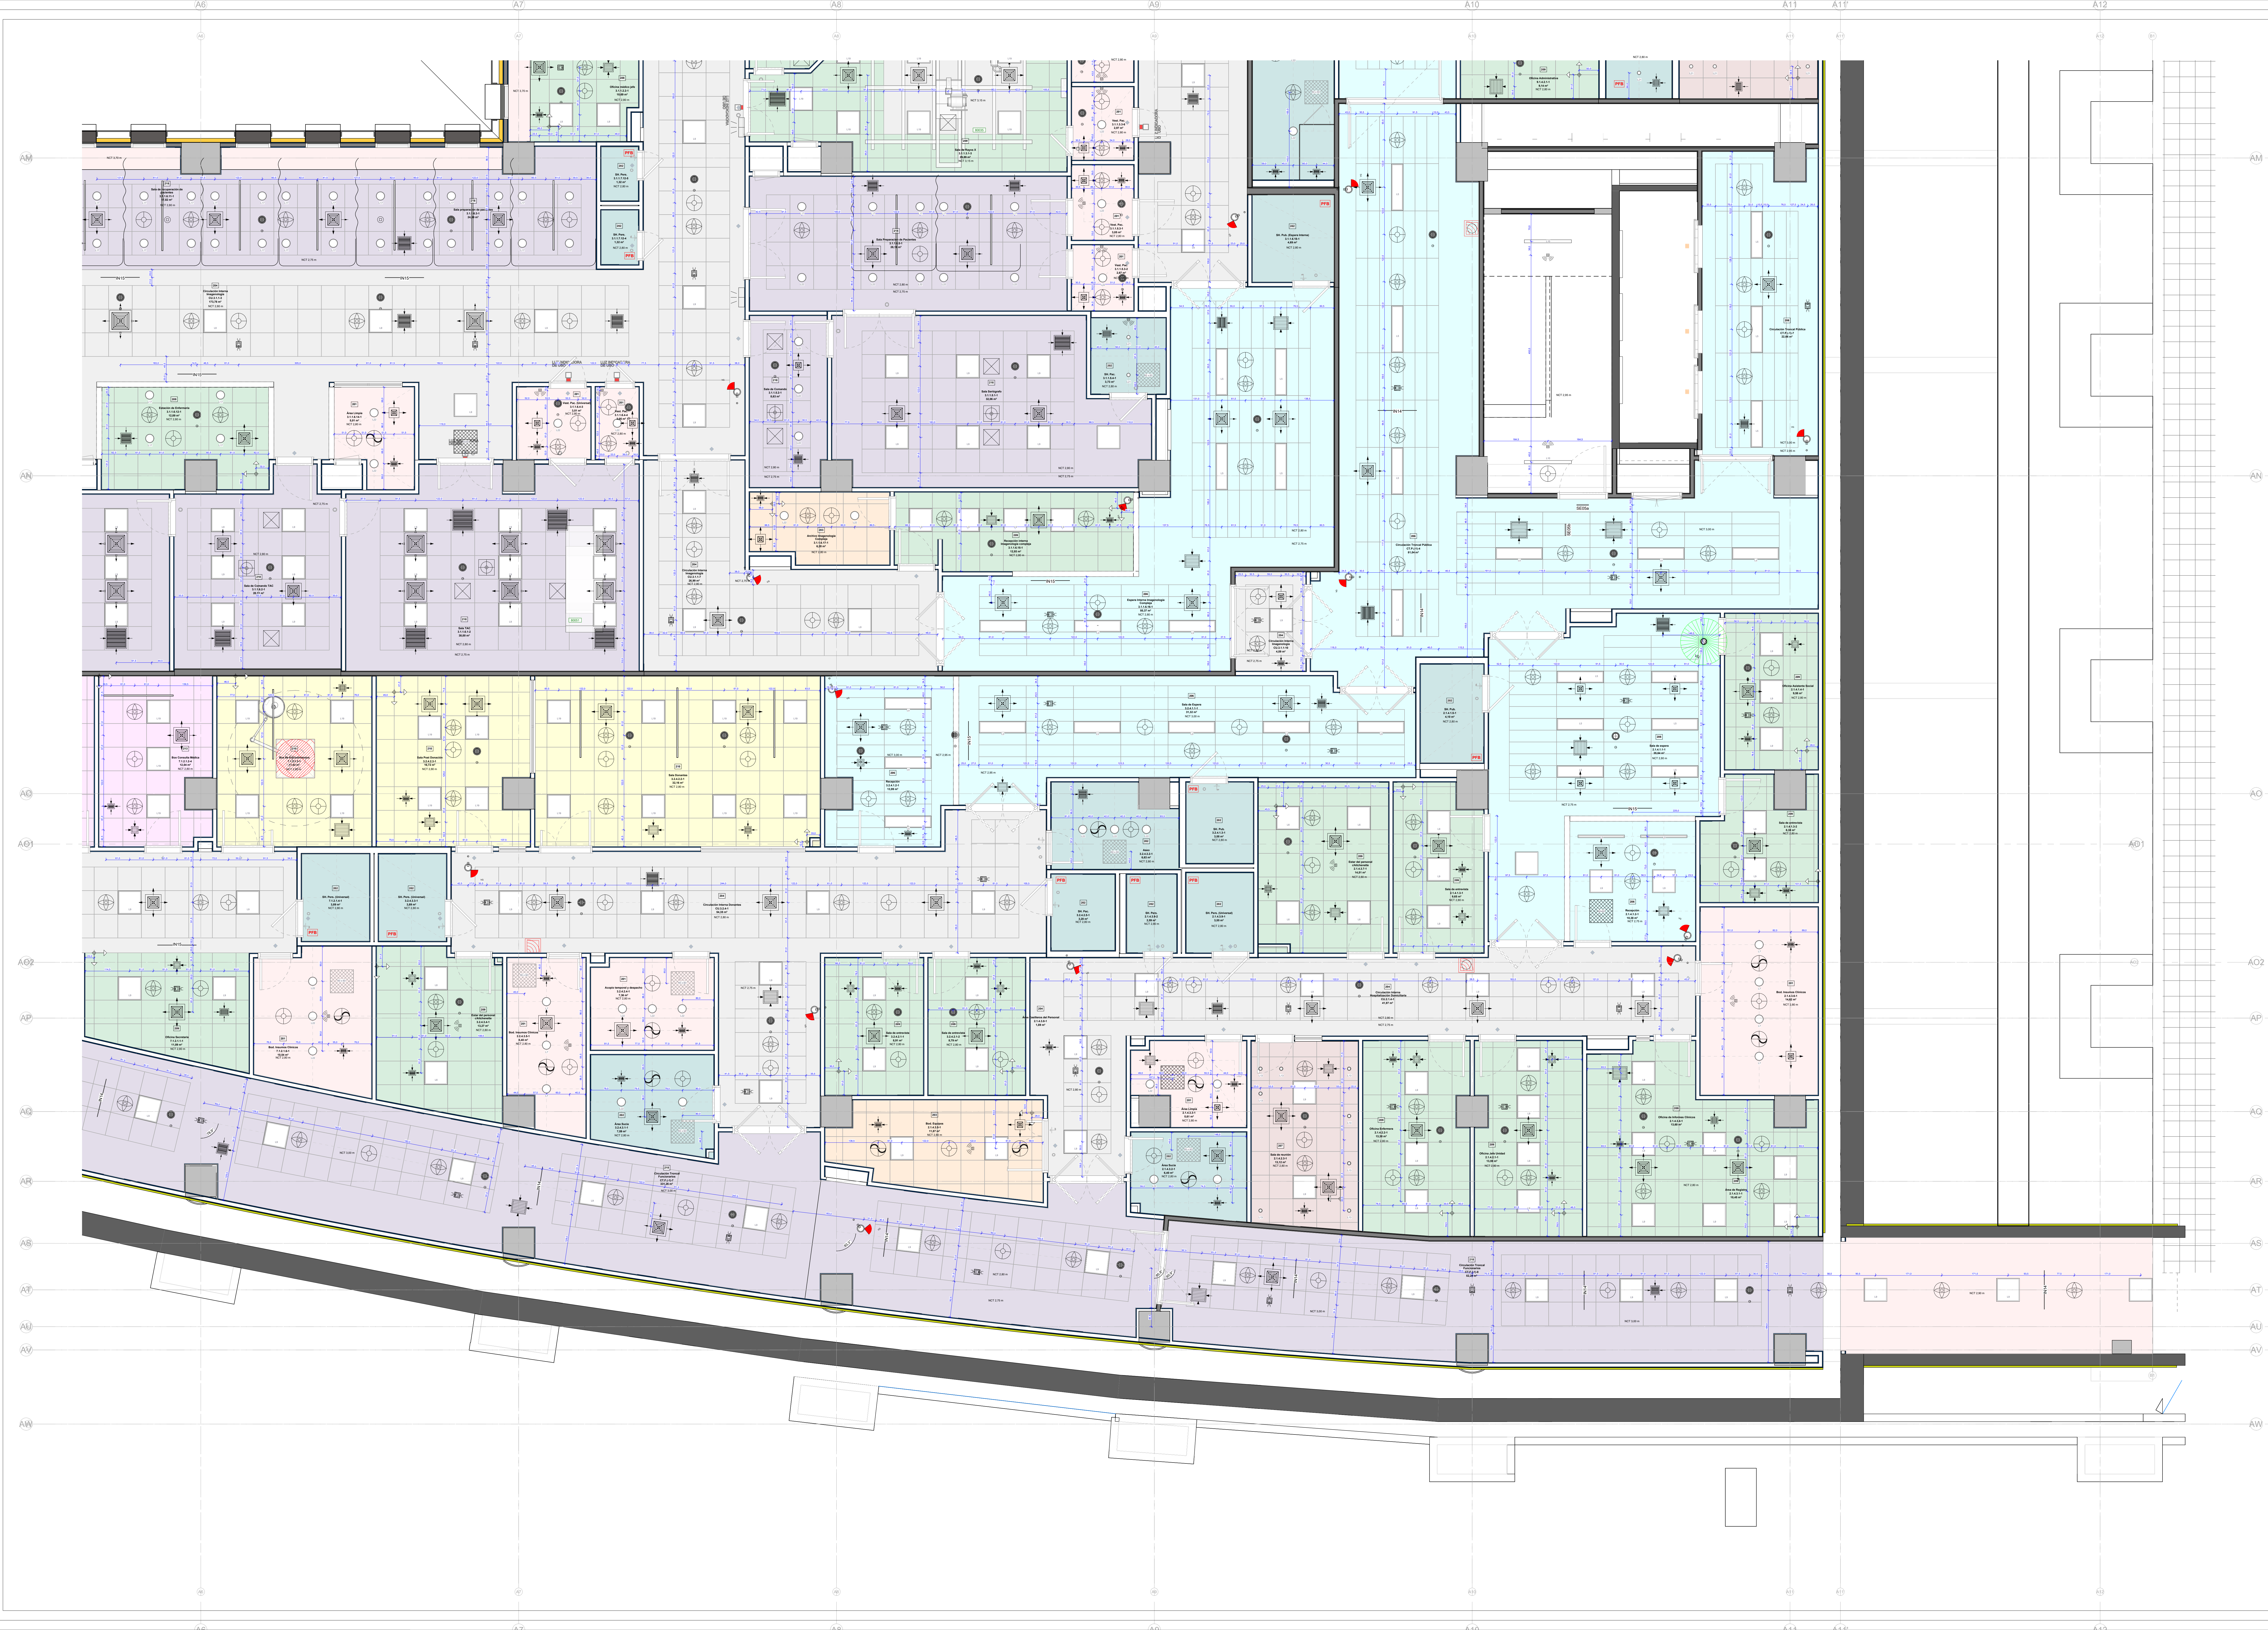

APTO PARA CONSTRUCCIÓN
HOSPITAL PROVINCIA CORDILLERA
sacyr INGENIERÍA E INFRAESTRUCTURAS

APROBADO
Por Sergio Fernandez fecha 9:52 , 07/11/2025

VERSIÓN 0
APTO PARA CONSTRUCCIÓN

Jonathan Cristopher Hervera Álvarez
Firmado digitalmente por Jonathan Cristopher Hervera Álvarez
Fecha: 2025.11.04 10:22:23 -03'00'

SIMBOLOGÍA CIELOS

200	□	Losa revocada en yeso para pintura
201	■	Cielo falso fijo de yeso-cartón, recintos secos (ST)
202	■	Cielo falso fijo de yeso-cartón, recintos húmedos (RH)
203	■	Cielo modular de yeso, revestido en vinilico de 24" y 48"
204	■	Cielo modular de yeso, revestido en vinilico c/cenefa
205	■	Cielo mixto modular de yeso. revestido en vinilo y cielo de yeso-cartón
206	■	Cielo modular acústico, bandeja chapa perforada metálica c/cenefa
207	■	Cielo modular de madera acústico
208	■	Cielo modular fibra mineral acústico
209	■	Cielo Acústico 1: Cielo modular acústico Owa flexo
210	■	Cielo Acústico 2: Cielo modular acústico Owa Humancare
211	■	Cielo Acústico 3: Cielo liso Volcanita acústica Rigitone 8-18
213	■	Cielo Acústico 4: Cielo modular acústico Owa Opus
214	▦	Cielo metalico exteriores + aislación
215	■	Cielo autoportante de panel PUR 100 mm
216	■	Cielo autoportante de panel PUR 70 mm
217	■	Cielo con placas termoaislantes con núcleo lana de roca y caras de acero galvanizado pre pintado 0,6 mm
218	■	C. modular acústico Owa Brillanto c/cenefa
219	■	Cielo mixto modular acústico Owa Humancare y cielo de yeso cartón
220	■	Cielo modular acústico Owa Opus c/cenefa
	▨	Aislación Térmica
	▨	Aislación Termo Acústica : Aislación + velo negro

SIMBOLOGÍA ILUMINACIÓN

○	L1	CORELINE LUZ EMPOTRABLE DELGADA DN145B/840	□	L23	PANEL GREENPERFORM RC160V W60L60
▭	L2	FLEXCOVE G3 LS170S Descripción se complementa con documento "HPC-4-ILU-GEN-INF-Luminaria hall entrada-01-RevA"	▭	L24	CORELINE ESTANCA G2 WT120C
▭	L3	FLEXCOVE G3 LS170S Descripción se complementa con documento "HPC-4-ILU-GEN-INF-Luminaria hall entrada-01-RevA"	◎	L25	LUMINARIA EXTERIOR EMPOTRADO EN MURO BBP341
▷	L4	LUMINARIA EXTERIOR EMPOTRADO EN MURO BBP341	▯	L25.1	LUMINARIA EXTERIOR EMPOTRADO EN PARED LED Step Light BWG150
▭	L5	GREEN PERFORM PANEL-W4 RC160V W30L120	⊞	L26	LUMINARIA EXTERIOR MONTAJE SOBRE ESTACA Essential SmartBright Spotlight BGP150
□	L6	PANEL GREEN PERFORM RC160V W60L60	▭	L27	LUMINARIA EXTERIOR ROADFLAIR BRP392
○	L7	CORELINE DOWNLIGHT DN140B	▭	L28	UNISTRIP G4 BCP382 L50
▭	L8	SLIMBALANCE SP550P LED 40S 840 L120 PSD CD GM	⊗	L29	CORELINE DOWNLIGHT DN140B
□	L9	PANEL GREENPERFORM RC160V W60L60	▭	L31	SMD3528 IP68
▭	L10	CORELINE ESTANCA G2 WT120C	◎	L32	LUMINARIA EXTERIOR EMPOTRADO EN PISO UNIIn-tierra BBP344
○	L11	GREENSPACE ACCENT CARDANIC RS343B	⊗	L33	LUMINARIA EXTERIOR TIPO BOLARDO LED Bollard II BCP150
▭	L12	SLIMBALANCE SP550P	○	L34	LUMINARIA EXTERIOR EMPOTRADO EN PISO UNIIn-tierra BBP344
○	L13	CORELINE RS141B	▭	L35	LUMINARIA EXTERIOR ROADFLAIR BRP392
▭	L14	FLEXCOVE G3 LS170S	○	L36	LUMINARIA EXTERIOR UNIURBAN BDP461
▭	L15	UNISTRIP G4 BCP382 L50	▭	L37	EQUIPO ESTANCO LED 15W MODELO: CORELINE WT1120 L600
▭	L16	CLEANROOM LED CR250B	◎	L38	FOCO EMPOTRABLE EN CIELO BIOLIMPIA
○	L17	CORELINE DOWNLIGHT DN140B	⊡	SL	SENSOR DE LUMINOSIDAD
▭	L18	GREEN PERFORM PANEL-W4 RC160V W30L120			SENSOR DE PRESENCIA
□	L19	CLEANROOM LED CR250B W60L60	SP-SL	SP-SL	SENSOR DE PRESENCIA Y LUMINOSIDAD
□	L20	PANEL GREENPERFORM RC160V W60L60			SENSOR DE PRESENCIA Y LUMINOSIDAD KNX O DALI
○	L21	CORELINE FOCO EMPOTRABLE RS141B			SENSOR DE PRESENCIA KNX O DALI
○	L22	CORELINE DOWNLIGHT DN140B			

SIMBOLOGÍA SEG - DETECCIÓN			**SIMBOLOGÍA CDE** - MEGAFONÍA Y SONIDO	
⊕	[1]	DETECTOR FOTOLÉCTRICO INTELIGENTE	⊕	ALTAVOZ DE EMPOTRAR 100V/6W
TF	[2]	DETECTOR DE CALOR DE TEMPERATURA FIJA	●	ALTAVOZ MÓVIL BIOLIMPIO 100V/6W
TV	[3]	DETECTOR DE CALOR DE TEMPERATURA VARIABLE	⊛	ALTAVOZ DE EMPOTRAR 32OHM/6W
☒	[6]	DETECTOR ÓPTICO DE HUMOS CONVENCIONAL		

SIMBOLOGÍA SEG - EXTINCIÓN			**SIMBOLOGÍA CDE** - CCTV	
⊕	[6]	Rociador Tipo1, ROCIADOR COLGANTE. K5,6, 68º, ½". SISTEMA HUMEDO. RIESGO LEVE	VG	CAMARA MINI DOMO (Vigilancia General)
⊕	[7]	Montante Tipo 2, ROCIADOR COLGANTE. K5,6, 68º DE ½". SISTEMA PREACCION. RIESGO LEVE	PB	CAMARA MINI DOMO (Pabellones)
⊕	[8]	Rociador Tipo 3, ROCIADOR COLGANTE. K5,6, 68º DE ½". SISTEMA HUMEDO. RIESGO ORDINARIO 1	PC	CAMARA MINI DOMO (Pacientes críticos, psiquiatría)
⊕	[10]	Rociador Tipo 4, ROCIADOR COLGANTE. K5,6 68º DE ½". SISTEMA HUMEDO. RIESGO ORDINARIO 2	VG	CAMARA MÓVIL EXTERIOR (Vigilancia general)
⊕	[12]	Rociador Tipo 5, ROCIADOR MONTANTE. K5,6, 68º DE ½". SISTEMA HUMEDO. RIESGO ORDINARIO 2	VG	CAMARA MÓVIL INTERIOR (Vigilancia general)
⊛	[13]	Rociador Tipo 6, ROCIADOR MONTANTE. K5,6, 68º DE ½". SISTEMA HUMEDO. RIESGO EXTRA 1	**SIMBOLOGÍA CDE** - DATOS	
⊕	[14]	Rociador Tipo 7, ROCIADOR COLGANTE 68º DE 1/2". SISTEMA HUMEDO. RIESGO ORDINARIO 2 (MISC.)	⊠	ANTENA WIFI
⊕	[15]	Rociador Tipo 8, ROCIADOR MONTANTE 68º DE 1/2". SISTEMA HUMEDO. RIESGO ORDINARIO 2 (MISC.)	⊡	ANTENA WIFI (RTLS)
⊛	[16]	Rociador Tipo 9, ROCIADOR COLGANTE 93º DE 1/2". SISTEMA HUMEDO. JAULA PROTECTORA	**DUCTOS DE EXTRACCIÓN EQU**	
⊕	[23]	Rociador Tipo 10, ROCIADOR MONTANTE 93º DE 1/2". SISTEMA HUMEDO. JAULA PROTECTORA	▨	MEDIDAS VARIABLES SEGÚN DUCTO
⊗	[24]	Rociador Tipo 11, ROCIADOR HORIZONTAL. K5,6 68º DE ½". SISTEMA HUMEDO. RIESGO ORDINARIO 2		
⊞	[38]	DIFUSOR COLGANTE EXTINCIÓN POR GAS		

SIMBOLOGÍA CLIMATIZACIÓN			**TAPAS DE REGISTRO**
⊠	DIF	DIFUSOR DE INYECCIÓN	▦ 40 x 40
▦	DIFL	DIFUSOR DE INYECCIÓN CON FILTRO ABSOLUTO HEPA	▦ 60 x 60
▣	DPP	DIFUSOR DE INYECCIÓN PLACA PERFORADA	
■	RE	REJILLA DE EXTRACCIÓN	
▤	RR	REJILLA DE RETORNO	
□	REF	REJILLA DE EXTRACCIÓN CON FILTRO ABSOLUTO HEPA	

SIMBOLOGÍA SEÑALETICA

IN10b	IDENTIFICADOR PARA PACIENTES TIPO 2 A CIELO
IN14	DIRECCIONAL ÁEREO
IN15	IDENTIFICATIVO ÁEREO
SE05a	IDENTIFICADOR COLGANTE DE SALIDA DE EMERGENCIA
SE05b	IDENTIFICADOR COLGANTE DE SALIDA DE EMERGENCIA

NOTAS

PFB: BAÑOS PREFABRICADOS
Los planos de cielos contemplan su coordinación y planos en DOSSIERS entregados a UT SSMSO.

CUADRO DE REVISIONES

REV.	FECHA	DESCRIPCIÓN
Rev00	13-02-2025	COORDINACIÓN DE CIELOS
Rev00_V1	19-08-2025	COORDINACIÓN DE CIELOS
Rev00_V2	11-09-2025	COORDINACIÓN DE CIELOS
Rev00_V3	30-09-2025	COORDINACIÓN DE CIELOS

Servicio de Salud Metropolitano Sur Oriente
Región Metropolitana
Ministerio de Salud

GOBIERNO DE CHILE
MINISTERIO DE SALUD
SERVICIO METROPOLITANO DE SALUD SUR-ORIENTE

DISEÑO Y CONSTRUCCIÓN HOSPITAL PROVINCIA CORDILLERA

ETAPA PROYECTO:
ETAPA DE OBRA

EMPLAZAMIENTO:

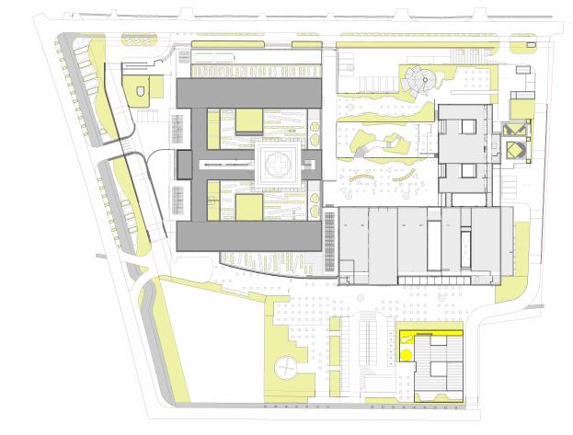

CONTRATISTA:
UTP SACYR HOSPITAL PROVINCIA CORDILLERA
sacyr INGENIERÍA E INFRAESTRUCTURAS

ARQUITECTO JEFE PROYECTO:
MARIANO ALVARO PRIETO LINDHOLM
Firmado digitalmente por MARIANO ALVARO PRIETO LINDHOLM
ALVARO PRIETO LINDHOLM
ARQUITECTO

FIRMA ITOs:
JONATHAN HERVERA ÁLVAREZ
INSPECTOR TÉCNICO DE OBRAS EN SALUD

ESPECIALIDAD:
ARQUITECTURA

CONTENIDO:
PLANTA COORDINACIÓN DE CIELOS -1-H

ORIENTACIÓN:

FECHA:	ESCALA:
30 SEPTIEMBRE 2025	1:50

LÁMINA:
HPC-ARQ-CIE-S01-A-508-Rev00_V3

ARCHIVO:
HPC-BIM-ARQ-GEN-XXX-AZ0-M2D-Rev00